


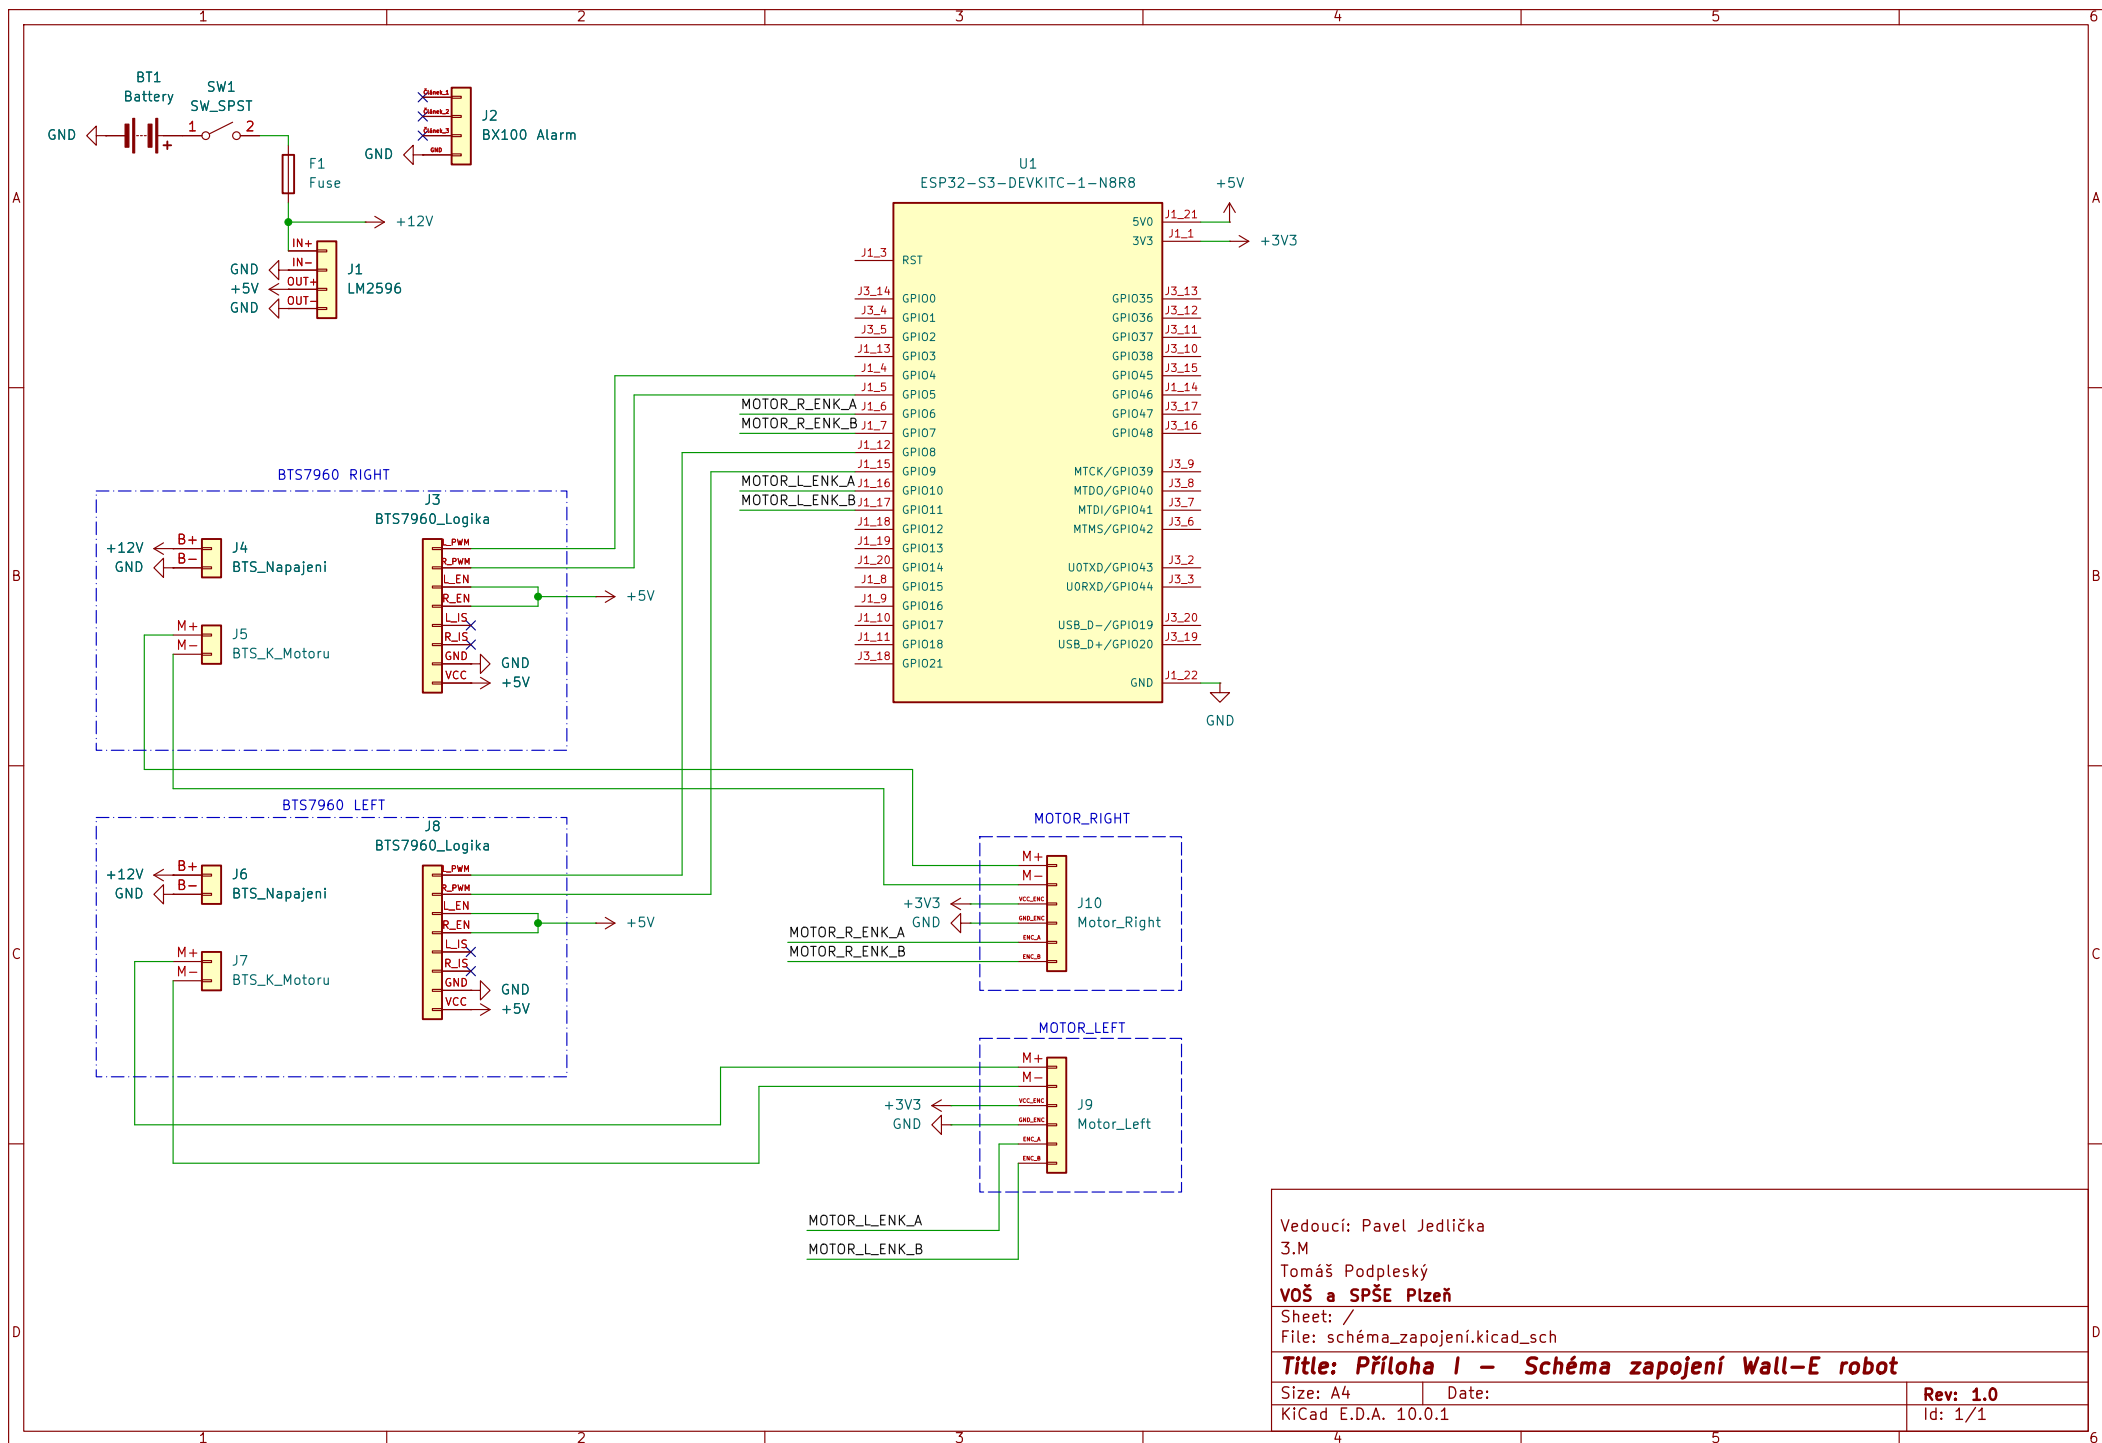

Vedoucí: Pavel Jedlička

3.M

Tomáš Podpleský

VOŠ a SPŠE Plzeň

Sheet: /

File: schéma_zapojení.kicad_sch

Title: Příloha I – Schéma zapojení Wall-E robot

Size: A4

Date:

Rev: 1.0

KiCad E.D.A. 10.0.1

Id: 1/1